10/8/25, 6:06 PM
18908355-CA66-4718-937B-6C7F2B0C87950B33CA48-FA9A-4226-A71B-029BD47EF1BE,1161064,,false,false,,7314

RPC 14

WALDEN'S REVISITED SUBDIVISION

Situated in the Township of Scioto, County of Delaware, State of Ohio and being part of Sublot "G" of Lot 1, Erasmus Gill's Virginia Military Survey No. 4267. Being a subdivision of 10.455 acres, being all of the remainder of an original 10.455 acre tract owned by Equity Trust Company Custodian FBO James B. Blumenstiel, IRA as recorded in Official Records Volume 1036, Page 409, and being all of an original 5.001 acre tract owned by John Ryan Boles and Elizabeth A. Boles as recorded in Official Records Volume 1387, Page 1223 in the Delaware County Recorder's Office.

Easements are hereby reserved, in, over, and under areas designated on this plat as "Drainage Easement", "Sanitary Easement", and "Utility Easement". Easements designated as "Drainage Easement" and "Utility Easement" permit the construction, operation, and maintenance of all public and quasi-public utilities above, beneath, and on the surface of the ground and, where necessary, for the construction, operation, and maintenance of service connections to all adjacent lots and lands and for storm water drainage.

Within those areas of land designated "Drainage Easement" on this plat, an additional easement is hereby reserved for the purpose of constructing, operating, and maintaining major storm water drainage swales and/or other above ground storm water drainage facilities. No above grade structures, dams, or other obstructions to the flow of storm water runoff are permitted within Drainage Easement areas as delineated on this plat. Easement areas shown hereon outside of the platted area are within lands owned by the undersigned and easements are hereby reserved therein for the uses and purposes expressed herein.

For any easement shown on this plat that contains a storm sewer, culvert, over land open ditch flood route, detention basin, retention basin and/or other storm water structure (herein referred to as storm sewer), the storm sewer rights are senior to the rights of any other public or private utility or interest utilizing the easement, except for overlap areas with a "Sanitary Easement". Any costs associated with the damage, repair, replacement or relocation of any buried or above ground facility or structure that is necessary to allow the maintenance, repair or replacement of the storm sewer shall be the responsibility of the owner of said utility, facility or structure. When maintenance, repair or replacement of a storm sewer causes the removal of any trees, plantings, landscaping, fence, driveway or any other feature located within the easement, the replacement and cost of said items shall be the responsibility of the owner of the underlying property or homeowner's association if applicable.

Any landscape features, such as trees, fences, retaining walls, etc. in Drainage Easements shall be reviewed by the Delaware County Soil and Water Conservation District (DCSWCD) and the Delaware County Engineer's Office (DCEO) prior to installation. The DCSWCD and DCEO will review the proposed improvements to assure that the improvements will not interfere with the storm water control facilities.

No buildings, sheds, decks, pools, or other structures, or the footers or foundations of any structures or features shall be constructed above or below ground within the limits of any Drainage Easements unless said structure is approved in writing by the Delaware County Engineer's Office.

We (I) the undersigned, being all the owners and lien holders of the land platted herein, certify that the attached plat correctly represents our (my) "WALDEN'S REVISITED SUBDIVISION", a subdivision of Lots 419 to 421 inclusive, do hereby accept this plat of same, do voluntarily consent to dedicate 0.083 acres for road right-of-way as shown hereon and not heretofore dedicated.

IN WITNESS THEREOF We (I) hereunto set our (my) hand(s) this 2nd day of June, 2016

SIGNED

Equity Trust Company Custodian FBO James B. Blumenstiel, IRA
Jeffrey S. Brown
Corporate Alternate Signer

STATE OF OHIO

Before me, a Notary Public, personally came the above named Jeffrey S. Brown Authorized Signatory for Equity Trust Company Custodian FBO James B. Blumenstiel, IRA, who acknowledged the signing of the foregoing instrument to be their voluntary act and deed for the uses and purposes as expressed.

IN WITNESS THEREOF, I have hereunto set my hand and affixed my seal this 2nd day of June, 2016

NOTARY PUBLIC — My Commission expires 4.28.19

BRANDI BORTNER
Notary Public, State of Ohio
My Commission Expires
April 28, 2019

PC 4 Sl. 45-45A

IN WITNESS THEREOF We (I) hereunto set our (my) hand(s) this 06 day of June, 2016

SIGNED

John Ryan Boles — Elizabeth A. Boles

STATE OF OHIO

Before me, a Notary Public, personally came the above named John Ryan Boles and Elizabeth A. Boles who acknowledged the signing of the foregoing instrument to be their voluntary act and deed for the uses and purposes as expressed.

IN WITNESS THEREOF, I have hereunto set my hand and affixed my seal this 10 day of June, 2016

NOTARY PUBLIC — My Commission expires MAY 22, 2019

DAVID TENG - NOTARY PUBLIC
COMM. EXP. MAY 22, 2019
STATE OF OHIO

APPROVED THIS 20 DAY OF June, 2016
SCIOTO TOWNSHIP ZONING INSPECTOR

APPROVED THIS 30 DAY OF June, 2016
DELAWARE GENERAL HEALTH DISTRICT

APPROVED THIS 22 DAY OF June, 2016
DEL-CO WATER CO., INC.

APPROVED THIS 1st DAY OF July, 2016
DELAWARE COUNTY SANITARY ENGINEER

APPROVED THIS 1st DAY OF July, 2016
DELAWARE COUNTY ENGINEER

APPROVED THIS 1ST DAY OF AUGUST, 2016
DELAWARE COUNTY REGIONAL PLANNING DIRECTOR

THIS 15th DAY OF August 2016, RIGHT-OF-WAY FOR ALL ROADS, BOULEVARDS, AND EASEMENTS HEREIN DEDICATED TO PUBLIC USE ARE HEREBY APPROVED AND ACCEPTED AS SUCH FOR THE COUNTY OF DELAWARE, STATE OF OHIO.

DELAWARE COUNTY COMMISSIONERS

TRANSFERRED THIS 16 DAY OF August, 2016
DELAWARE COUNTY AUDITOR

Doc ID: 011182390002 Type: OFF
Kind: PLAT
Recorded: 08/16/2016 at 11:03:12 AM
Fee Amt: $80.00 Page 1 of 2
Workflow# 0000124013-0001
Delaware County, OH
Melissa Jordan County Recorder
File# 2016-00024048
BK 1443 PG 1516-1517

AY OF _____, 2016
_____, PAGE _____
G NO. _____
Melissa Jordan
ORDER

SURVEYED AND PLATTED BY
KAREN S. COFFMAN, SURVEYOR REG. No. 7845

SCIOTO LAND SURVEYING SERVICE, INC.
173 North Sandusky Street Delaware, Ohio 43015 740.369.7577 karen@sciotolandsurveying.com

https://delaware.dts-central-oh.com/PaxWorld/web/printViewer.ht...-4226-A71B-029BD47EF1BE%2C1161064%2C%2Cfalse%2Cfalse%2C%2C7314

WALDEN'S REVISITED SUBDIVISION

RPC 14-16

PART OF SUBLOT G OF LOT 1,
ERASMUS GILL'S VIRGINIA MILITARY SURVEY NO. 4267
SCIOTO TOWNSHIP, DELAWARE COUNTY, OHIO
ALL OF THE REMAINDER OF AN ORIGINAL 10.455 Ac., O.R.V. 1036, PG. 409, &
ALL OF AN ORIGINAL 5.001 Ac., O.R.V. 1387, PG. 1223

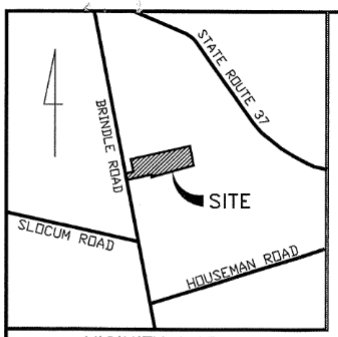

VICINITY MAP

SETBACKS
FRONT – 90' FROM CENTERLINE OF CAD – 50' FROM WIDENING
SIDE – 25'
REAR – 80' (15' ACCESSORY BLDG)

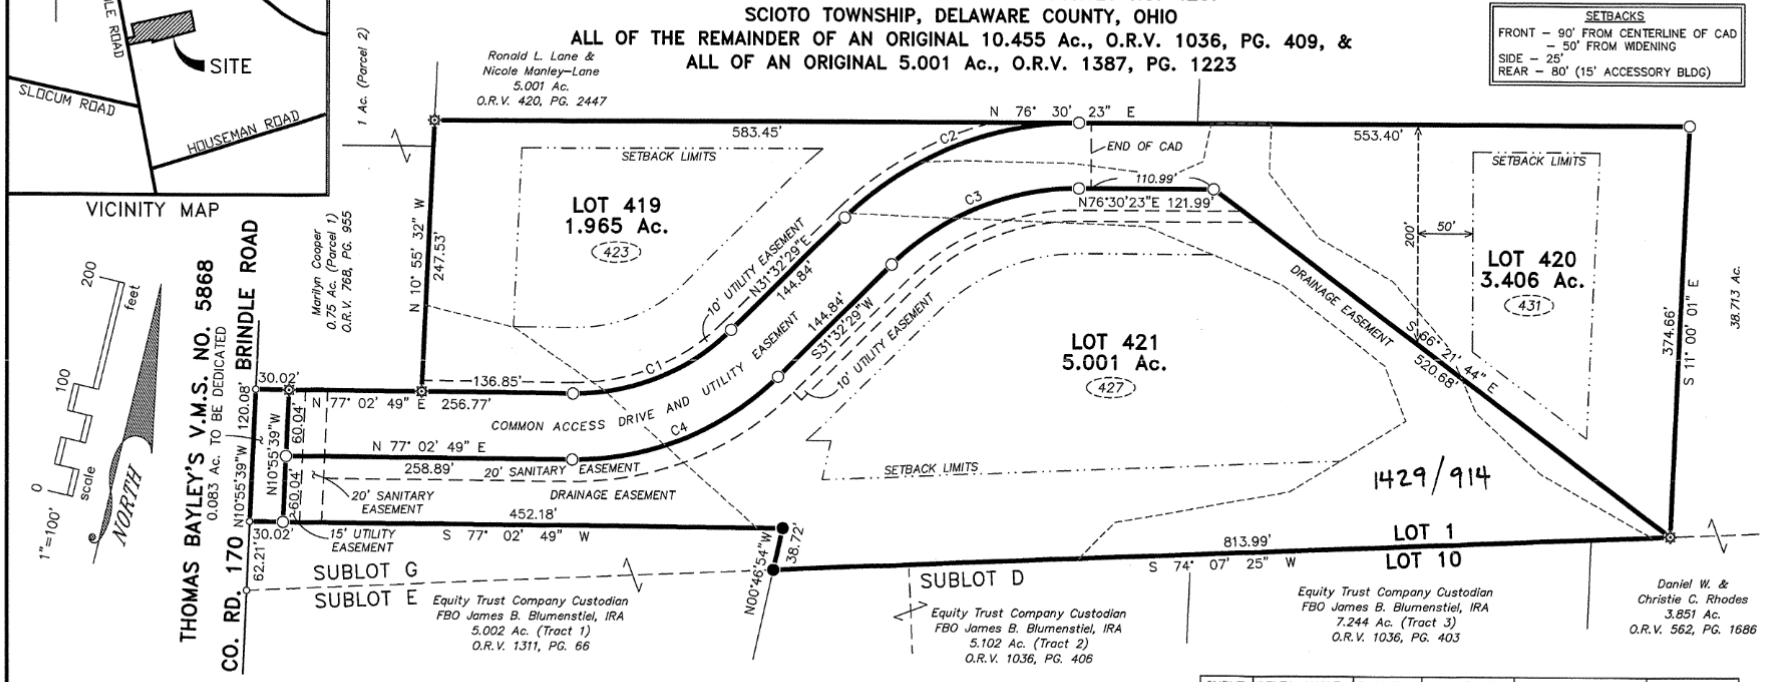

CURVE	DELTA ANGLE	RADIUS	ARC LENGTH	CH. BEARING	CH. LENGTH
C1	45° 30' 21"	200.00'	158.84'	N 54° 17' 39" E	154.70'
C2	44° 57' 55"	300.00'	235.44'	N 54° 01' 26" E	229.44'
C3	44° 57' 55"	240.00'	188.35'	S 54° 01' 26" W	183.55'
C4	45° 30' 21"	260.00'	206.50'	S 54° 17' 39" W	201.11'

The owners, their successors, heirs or assigns of the herein delineated lots agree that when a central sewage system becomes available, said lot shall be connected to said central sewer system. Acceptance of title to a delineated lot for the subdivision shall constitute waiver of further notice of hearing on this requirement. This covenant shall be included in conveyance of title for said lots.

Roof drains, foundation drains and other clean water connections to the sanitary sewer system are prohibited.

All Lots shall take access from the Common Access Drive and NOT directly from Brindle Road.

The earthwork contractor shall comply with the "Delaware County Urban Sediment Pollution and Water Run-off Control Regulations" as adopted by the County Commissioners.

A non-exclusive easement is hereby specifically granted unto Del-Co Water Company, Inc., its successors and assigns, for the location of water lines, valves, and appurtenances within the rights-of-way hereby dedicated and within areas designated hereon as "Common Access Drive and Utility Easement" or "Utility Easement" or "Drainage Easement" that are located alongside the rights-of-way hereby dedicated. Also granted is the right of Del-Co Water Company, Inc. to install, service, and maintain water meter crocks and appurtenances in said easement areas alongside said rights-of-way.

Easements are reserved for the construction, operation and maintenance of all public and private utilities proposed above and beneath the surface of the ground, and where necessary, are for the construction, operation and maintenance of service connections to all lots and lands, and for storm water drainage.

Easements designated as "Sanitary Easement" shall mean a perpetual, exclusive sanitary easement over, through, under, within, upon, and across the area herein delineated, together with ingress and egress over reasonable routes across Grantor's tracts that adjoin the easement area when exercising the purposes of this easement, solely for construction, operation and maintenance of public and or private sanitary sewers, sanitary sewer service connections, sanitary force mains, sanitary manholes, sanitary valves, and other sanitary appurtenances.

No other utility shall be located within the sanitary easement except for crossings as described herein; right angle or near right angle utility crossings ("near right angle" is defined as an angle between eighty (80) degrees and one-hundred (100) degrees) over, across, or under the sanitary line and over, across, under, or through this sanitary easement are not restricted, except that all utility crossings under the sanitary sewer or force main shall be subject to the review and approval of the Delaware County Sanitary Engineer; any utility crossing within the sanitary easement resulting in an angle less than 80 degrees shall only be permitted if approved in writing by the Delaware County Sanitary Engineer.

No buildings, sheds, decks, pools, or other such structures, or the footers or foundations of any structures or features shall be constructed above or below ground within the limits of the sanitary easement unless said structure is approved in writing by the Delaware County Sanitary Engineer; any landscaping features, such as, but not limited to, trees, fences, signs, retaining walls, etc., within the sanitary easement area shall be reviewed for approval by the Delaware County Sanitary Engineer prior to installation; any landscaping features placed within the sanitary easement may be removed at any time by the Delaware County Sanitary Engineer or his/her representatives; the cost of restoration shall be the responsibility of the Grantor, or, upon conveyance by the Grantor, by the Grantor's successors and assigns.

The addition or removal of any dirt, soil, fill, or other changes to the ground elevation above the sanitary sewer or force main within the sanitary easement shall be subject to approval of the Delaware County Sanitary Engineer; the Delaware County Sanitary Engineer reserves the right to require that all earthwork within the sanitary easement be graded to such a level that will, in his or her opinion, not jeopardize the structural integrity of or limit the County's reasonable access to the sanitary sewer or force main.

Prior to preparation of building plans and/or detailed site plans, each lot owner must coordinate with the Delaware County Health Department to determine that the approved on-site sewage treatment system location is consistent with or compatible with the owner's desired site plan.

Notice is hereby given to any buyer of the lots delineated upon this plat, that on file with the Delaware County Regional Planning Commission, and Health Department are SITE IMPROVEMENT PLANS for the development of said lots showing finish grade elevations, sewage treatment system locations, and building envelopes.

All lots are located in Flood Zone "X" per Community Panel No. 390146 0080 K, dated April 16, 2009.

BE ADVISED: A sub-surface drainage system may exist on this site. The system and/or outlet if located on this property must be maintained at all times.

Approval of this plat by the Delaware County Regional Planning Commission, the Delaware County Commissioners and/or any other governmental authority shall in no way constitute a dedication or acceptance of the Common Access Drive shown thereon, and all such Common Access Drive(s) shall be and remain a private access way, and the Delaware County Regional Planning Commission, the Delaware County Commissioners and every other public authority signing this plat shall have no responsibility or liability for or arising out of the construction, improvement, maintenance and/or use of any such Common Access Drive. The owners of these lots and their successors and assigns agree to and shall be bound by the foregoing provision, which provision shall be deemed to be and is a covenant running with the land.

C.A.D. MAINTENANCE AGREEMENT RECORDED IN
O.R.V. 1429 PG. 909

Drainage Maintenance Petition Recorded
in the Delaware County Commissioner's Journal,
Resolution No. 16-795 Journal Date 8/15/16

OWNERS & DEVELOPERS:
Equity Trust Company Custodian
FBO James B. Blumenstiel, IRA
225 Burns Road
Elyria, Ohio 44035

AND:

John Ryan Boles & Elizabeth A. Boles
8364 Squad Drive
Galloway, Ohio 43119

(423) HOUSE NUMBER

LEGEND
- ● 3/8" Iron Bar Found
- ✪ 3/4" Iron Pipe Found
- ○ MAG Nail Set
- ○ 5/8" Iron Bar Set with a plastic cap marked "SLSS PS 7845"

RECORDS USED
Deeds as shown.

BASIS OF BEARINGS
Centerline of Brindle Road per O.R.V. 1036, Page 409 (N 10° 55' 39" W)

STATE OF OHIO
KAREN S. COFFMAN 7845
REGISTERED PROFESSIONAL SURVEYOR

I HEREBY CERTIFY THAT I HAVE SURVEYED THE PROPERTY DESCRIBED IN THE FOREGOING TITLE CAPTION AND THAT SAID SURVEY AND SKETCH ARE ACCURATE AND CORRECT TO THE BEST OF MY KNOWLEDGE AND BELIEF, EASEMENTS, RESTRICTIONS AND RIGHTS-OF-WAY, IF ANY, NOT LOCATED UNLESS NOTED.

KAREN S COFFMAN, SURVEYOR
Registration No. 7845

APRIL 11, 2016
Date of Survey

ORIGINAL PARCELS ACREAGE: 10.455 ACRES
TOTAL SUBDIVISION ACREAGE: 10.455 ACRES
ACRES REMAINING: 0 ACRES
ACREAGE IN 3 LOTS: 10.372 ACRES
ACREAGE TO BE DEDICATED: 0.083 ACRES
ACREAGE IN CAD: 1.113 ACRES
DEVELOPMENT DENSITY = 0.29 UNITS PER ACRE

SCIOTO LAND SURVEYING SERVICE, INC.
173 North Sandusky Street Delaware, Ohio 43015 740.369.7577 karen@sciotolandsurveying.com